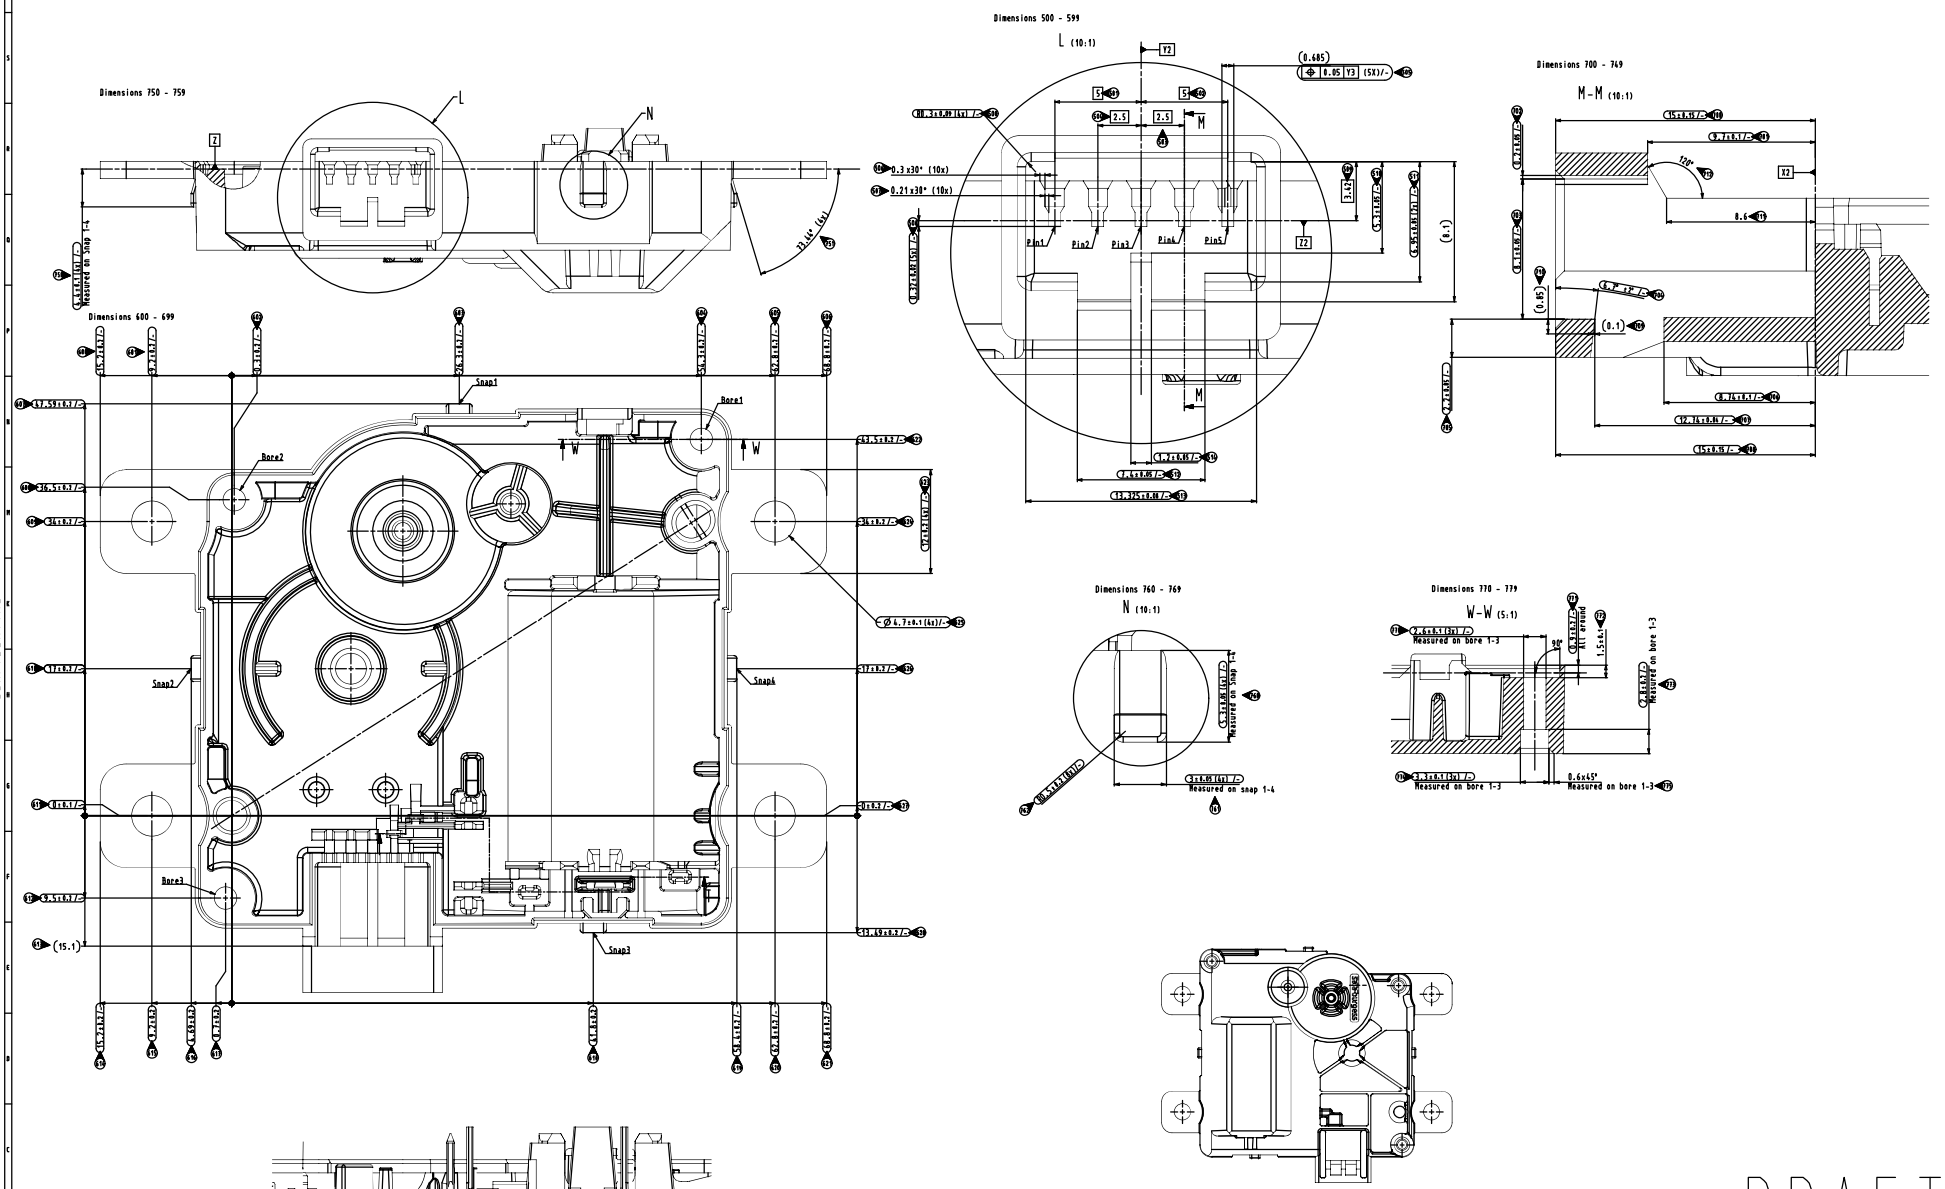


DRAFT

17.05.2024

DRAWN	11-Apr-2024 N. Bertie	TOLERANCES	-
APPROVED		MATERIAL	see Table on the drawing
CHANGE			
STATUS	-	SCALING	5:1
TITLE	Housing V1		mm
ID	D0601144068		SH. 1/2
			REV. A

CONFIDENTIAL